



Numri i Protokollit

188/2020

Republika e Kosovës
Republika Kosova-Republic of Kosova
Qeveria -Vlada-Government

Ministria e Mjedisit dhe Planifikimit Hapësinor /Ministarstvo Sredine i Prostornog Planiranja/Ministry of Environment and Spatial Planning
AGJENCIA KADASTRALE E KOSOVËS/ KATASTARSKA AGECA KOSOVA/ KOSOVA CADASTRAL AGENCY

Formulari nr. 5

KËRKESË PËR SHERBIMET KADASTRALE NGA GJEODETI APO KOMPANIA GJEODETE E LICENCUAR

Gjeodeti / Kompania gjeodete e licencuar: Liridon Sejdiu	Numri i licencës: 140
--	-----------------------

Komuna: Ferizaj	Zona Kadsatrale: Prelez i Muaxhereve
-----------------	--------------------------------------

Numri i njësisë kadastrale: 00525-0

1. Të dhënrat për parashtruesin e kërkesës

Emri / Emri i Kompanisë: Mehdi	Mbiemri: Jakaj	Emri i prindit: Isuf
Numri personal: 1003798352	Adresa: Fsh. Prelez i Muaxherev - Ferizaj	Nr. Tel: +383 44 311 621
Numri i biznesit: (për person juridik dhe kompani)		

2. Parashtruesi i kërkesës: Pronar - Shfrytëzues - Përfaqësues i Autorizuar

3. Lista e dokumenteve të nevojshme:

Pronari/Shfrytëzuesi	Përfaqësues i Autorizuar
1 <input checked="" type="checkbox"/> Letërnjoftimin / Certifikatë biznesi (kopje)	1 <input type="checkbox"/> Letërnjoftimin / Certifikatë biznesi (kopje)
2 <input checked="" type="checkbox"/> Vërtetimi i tatimit në pronë	2 <input type="checkbox"/> Vërtetimi i tatimit në pronë
3 <input type="checkbox"/> Çertifikata e pronës	3 <input type="checkbox"/> Çertifikata e pronës
4 <input type="checkbox"/> Kopja e planit	4 <input type="checkbox"/> Kopja e planit

4. Kërkesa për:

1 <input type="checkbox"/> Ndërrim të kulturës së parcelës	6 <input type="checkbox"/> Matjen dhe regjistrimin e ndërtesës
2 <input checked="" type="checkbox"/> Ndarjen e parcelës	7 <input type="checkbox"/> Matjen dhe regjistrimin e pjesës së ndërtesës
3 <input type="checkbox"/> Bashkimin e parcelës	8 <input type="checkbox"/> Punë të veçanta gjeodezike
4 <input type="checkbox"/> Përcaktimin e kufijve të parcelës	9 <input type="checkbox"/> Matja e ndërtesës për legalizim
5 <input type="checkbox"/> Ri-regullimin e kufirit të parcelës	10 <input type="checkbox"/> Riregjistrim i pjesës grafike

Nënshkrimi: Mehmet Sejdiu
Data: 21.08.2020



REPUBLIKA E KOSOVËS - REPUBLIKA KOSOVA - REPUBLIC OF KOSOVA

KOMUNA FERIZAJ - OPŠTINA UROŠEVAC - MUNICIPALITY OF FERIZAJ



DEFTESE-PRIZNANICA

NF/FN/NB600629804

Nr. Serik/ Ser Br./ Ser No
063555

1174982178

Numri Personal / Licni Broj

Liridon Sejdiu

Pagoi / Isplatio

Lloji i Pageses / Splacajna

Kerkese per blerjen e produkteve

Pershkrimi / Opis

Adresa e vendosur:

Greme

Numri i tel. fiks

Numri i tel. mobil

2. Mënyra e pranimit

Statusi i lëndës

Kërkesa

Ne proces

3. Ju lutemi të shkruani kërkesën apo ankesën tuaj në detaje:

Kerkese per blerjen e produkteve kadastrale /parc.nr.525-0 ZK Prelez i M.

10.00

Shuma / Iznos

10-942/05-0067190/20

Numri i Protokolit / Broj Protokola

21/08/2020

Data / Datum

Lebibe.Sadiku

Arketari / Blagojnik

Nenshkrimi / Potpis

Vendimi

Vlera për pagesë: 10.00

4. Dokumentet e bashkangjitura:

Nr. Lloji i dokumentit

5. Dëshmia e aplikuesit për vërtetësi

Unë Liridon Sejdiu vërtetoj se informata e lartshënuara janë të vërteta.

(Nënshkrimi)

*Ju lutemi të kérkonit nga zyrtari/ja fletëdëshminë për dorëzimin e kësaj kërkeze dhe dokumenteve të bashkangjitura

Pranuar nga: Fitnate.Bajrami



Republika e Kosovës

Republika Kosova - Republic of Kosovo

Qeveria e Kosovës - Vlada Kosova - Government of Kosovo

Ministria e Infrastrukturës dhe Ambientit/ Ministrastvo Infrastrukture i Sredine/ Ministry of Infrastructure and Environment

AGJENCIA KADASTRALE E KOSOVËS/ KOSOVSKA KATASTARSKA AGENCIJA/ KOSOVA CADASTRAL AGENCY

MBËSHTJELLËS I LËNDËS

Gjeodeti / Kompania gjeodete e licencuar: **LIRIDON SEJDIU**

Numri i licencës: **140**

Numri i Protokollit: **188/2020**

LËNDA:

1. Ndërrim të kulturës së parcelës
2. Ndarjen e parcelës
3. Bashkimin e parcelës
4. Përcaktimin e kufijve të parcelës
5. Ri-rregullimin e kufirit të parcelës
6. Matjen dhe regjistrimin e ndërtesës
7. Matjen dhe regjistrimin e pjesës së ndërtesës
8. Regjistrimi i servitutit
9. Punë të veçanta gjeodezike
10. Matja e ndërtesës për legalizim

“GJEODET I LICENCUAR”

+383 49 535 250

e-mail: liridonsejdiu88@gmail.com

Data: **25/08/2020**

Vendi: **FERIZAJ**

.....

(Nënshkrimi dhe vula)

Përbajtja:

- Kërkesa e palës
 - Dëshmia e burimit të të dhënave zyrtare
 - Dëshmia e pagesës për të dhënat e pranuara
 - Fatura apo kuponi fiskal e lëshuar shërbimet kadastrale sipas UA 11/2019 dhe 12/2019
 - Procesverbali nga terreni
 - Manuali i njësive kadastrale
 - Regjistri i ndërrimeve
 - Lista e koordinatave të matura
 - Formulari i korrigjimit të sipërfaqes
 - Leternjoftimi i pronarit
 - Certifikatën e pronësisë
 - Raporti teknik
 - Leternjoftimi kopje i fqinjëve
 - Dokumentacioni i gjeodetit të licencuar

Dokumente tjerar:



Data e lëshimit / Датум издавања / Date of issue
21.03.2019

Lëshuar nga / Издат од / Issued by

MPB / MUP / MIA

Nr. Personal / Лични број / Personal No

1003798352

Nr. Lni. / Број Л.К. / ID Card No

ID1239708

Vendbanimi / Побудбиналиште / Residence

PRELEZ I MUHAXHERËVE, FERIZAJ

IDRKSID12397085 <<<<<<<<<<<
5503067M2903208RKS1003798352 <4
JAKA J <<MEHDI <<<<<<<<<<<



REPUBLIKA E KOSOVËS
РЕПУБЛИКА КОСОВО
REPUBLIC OF KOSOVO



Mbiem/Презиме/Name

JAKAJ

Eimi/Ime/First name

SALI

Gjimia/Пол/Sex

M

Data e lindjes/Датум рођења/Date of birth

02.05.1946

Vendi i lindjes/Место рођења/Place of birth

PRELEZ I MUHAXHERËVE

Data e skadimit/Датум истека/Date of expiry

Përhershëm/Trajna/Permanent

Data e leshimit/Датум издавања/Date of issue

01.03.2011

Leshuar nga/Служба која издаје/Issuing authority

MPB / MUP / MIA

Numri personal/Лични број/Personal number


1003798565

QKRC/OŠIP/MCRC

2501S

Nr.Inj/Бр.ак/Id.no

ID03429158

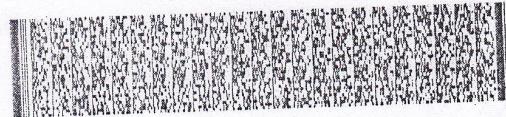



Republika e Kosovës / Republika Kosova / Republic of
Komuna e FERIZAJ / Opština UROŠEVAC / Municipality



Bazuar në nenin 18 të ligjit 03/L-204 për tatimin në pronë, si dhe udhëzimit administrativ nr. 7/2011 të lëshuar nga MF, i cili ka të bëjë me urdhëresat e ndalimit të shërbimeve komunale për detyrim të pagesës së tatimit në

Na osnovu člana 18, zakona 03/L-204 za poreza na imovinu i administrativne uredbe MF br. 7/2011, u vezi zabrane opštinskih usluga za prinudu uplate poreza na imovinu, izdaje se ova:

Based on the article 18 of LAW 03/L-204 on property tax and administrative instruction MF no. 7/2011 on termination of services for enforcement of the municipal property tax, the municipal Property Tax Office

Nr / Br / No

21/08/2020

22514897

VËRTETIM POTVRDA CERTIFICATE

Me të cilin vërtetohet se tatimpaguesi
Kojim se potvrđuje da je poreznik
that certifies that taxpayer

SALI JAKAJ

FERIZAJ

Komuna / Opština / Municipality

FERIZAJ

adresa / adresa / address

I ka kryer pjesërisht / plotësisht obligimet e tatimit në pronë
Delimično/ izveršio uplatu poreskih obaveza
has partially / fulfilled obligations on property tax

SALI ISUF JAKAJ

Vërtetimi lëshohet në bazë të kërkesës së / Potvrda se izdaje na zahev / Certificate is issued by

Për nevoja personale

dhe shërben për / i služi za / and is used for

Shënime shtesë / Druge podatke / Additional info





Republika e Kosovës

Republika Kosova-Republic of Kosovo
Qeveria - Vlada - Government

MINISTRIA E EKONOMISË DHE AMBIENTIT / MINISTARSTVO EKONOMIJE I ŽIVOTNE SREDINE / MINISTRY OF ECONOMY AND ENVIRONMENT
AGJENCIA KADASTRALE E KOSOVËS / KATASTARSKA AGENCIJA KOSOVA / KOSOVO CADASTRAL AGENCY

CERTIFIKATË / CERTIFIKAT / CERTIFICATE

PERSONI / OSOBA /PERSON : JAKAJ SALI

66937-2020

21.08.2020 - 10:38

Ferizaj / Uroševac / Ferizaj
Ferizaj / Uroševac / Ferizaj

Komuna / Opština / Municipality:

Zyra Kadastrale Komunale / Opštinska Katastarska Kancelarija / Municipal Cadastral Office:

A. TË DHËNAT PËR PERSONIN / PODACIO OSOBI / PERSON'S DATA

Mbiemri/Emri i afarizmit (biznesit) Prezime/ Naziv poslovanja (biznisa) Last Name / Business Name	Emri i babait Ime oca Father's Name	Gjinia Pol Gender	Nr. personal/ biznesit Lični broj/broj poslovanja ID. No.	Shfeti i shtetësisë apo regjistrimit Država državljanstva ili uknjiženja Country of citizenship	Ditëlindja/Data e themelimit Rodëdan/Dan osnivanja Date of Birth/Establishmen t	Krijuar më datën Uradjeno na dan Created On	Azhuruar Ažurirano Updated
JAKAI	SALI	ISUF	Mashkull / Musko / Male	1003798565	KOSOVA / KOSOVA / KOSOVO	02.05.1946	27.08.2014

A.1 ADRESA E PERSONIT / ADRESA OSOBE / PERSON'S ADDRESS

Vendbanimi Prebivaliste Resident	Kodi Postal Poštanski Kod Postal Code	Hollësitë e adresës Pojedinitë adrese Address Details	Adresa tjetër Druga adresa Other address
PRELEZ I MUHAXHERËVE / MUHADŽER PRELEZ / PRELEZ I MUHAXHERËVE			Azhuruar Ažurirano Updated



B. NJESIA KADASTRALE/ KATASTARSKA JEDINICA/CADASTRAL UNIT

Njësie kadastrale Katastarska jedinica Cadastral unit	Komuna / Opština / Municipality	Zona kadastrale Katastarska zona Cadastral zone	Lloji i njësisë Vrsta jedinice Unit type	Tipi i pronës Tip imovine Property Type	Kati/ Katet Br.Sprat a/ Spratova Floor number	Vendi i quajtur Zvano mesto Place name	Sipërfaqja Površina Area	Shfrytezimi aktual/Kultura- upotreba/ Kultura-klaša Actual use/Culture-class	Pjesa e pronës Deo imovine Share quota	Lloji i së drejtës Vrsta prava Type of the right	Azhuruar Ažurirano Updated
P-72209060-00327-0	Ferizaj / Uroševac / Ferizaj	PRELEZ I MUHAXHERË VE / MUHADŽER PRELEZ / PRELEZ I MUHAXHERË VE	PARCELË / PARCELA / parcel	Proni private Privatna Imovina Privately owned Land /	ANA E PRELEZIT / ANA E PRELEZIT / ANA E PRELEZIT	240	Bujqësore - Arat - Arë E Klasës 3 / Poljoprivredno - Njive - Njiva 3 Klase / / Agriculture - Arable - 3rd Class Arable Land / /	1 / 1	Posedim individual / Individualna Drzavina / single possessor		
P-72209060-00328-0	Ferizaj / Uroševac / Ferizaj	PRELEZ I MUHAXHERË VE / MUHADŽER PRELEZ / PRELEZ I MUHAXHERË VE	PARCELË / PARCELA / parcel	Proni private Privatna Imovina Privately owned Land /	ANA E PRELEZIT / ANA E PRELEZIT / ANA E PRELEZIT	280	Bujqësore - Arat - Arë E Klasës 3 / Poljoprivredno - Njive - Njiva 3 Klase / / Agriculture - Arable - 3rd Class Arable Land / /	1 / 1	Posedim individual / Individualna Drzavina / single possessor		
P-72209060-00352-0	Ferizaj / Uroševac / Ferizaj	PRELEZ I MUHAXHERË VE / MUHADŽER PRELEZ / PRELEZ I MUHAXHERË VE	PARCELË / PARCELA / parcel	Proni private Privatna Imovina Privately owned Land /	ANA E PRELEZIT / ANA E PRELEZIT / ANA E PRELEZIT	6320	Bujqësore - Arat - Arë E Klasës 4 / Poljoprivredno - Njive - Njiva 4 Klase / / Agriculture - Arable - 4th Class Arable Land / /	1 / 1	Posedim individual / Individualna Drzavina / single possessor		
P-72209060-00525-0	Ferizaj / Uroševac / Ferizaj	PRELEZ I MUHAXHERË VE / MUHADŽER PRELEZ / PRELEZ I MUHAXHERË VE	PARCELË / PARCELA / parcel	Proni private Privatna Imovina Privately owned Land / R	RANJA RRUGA FERIZAJT / RANJA RRUGA FERIZAJT / RANJA RRUGA FERIZAJT	7785	Bujqësore - Arat - Arë E Klasës 2 / Poljoprivredno - Njive - Njiva 2 Klase / / Agriculture - Arable - 2nd Class Arable Land / /	1 / 1	Posedim individual / Individualna Drzavina / single possessor	07.07.2015	







Republika e Kosovës
Republika Kosova-Republic of Kosova
Qeveria -Vlada-Government
Ministria e Mjedisit dhe Planifikimit Hapësinor /Ministarstvo Sredine i Prostornog Planiranja/Ministry of Environment and Spatial Planning
AGJENCIJA KADASTRALE E KOSOVËS/ KATASTARSKA AGECIJA KOSOVA/ KOSOVA CADASTRAL AGENCY

Zyra kadastrale komunale / Opštinska katastarska kancelarija: Ferizaj

Nr. i njësisë kadastrale / Br. katastarske jedinice : 525-0


Zona kadastrale / Katastarska zona: Prelez i Muhaxherëve

Numri i lëndës / Broj predmeta: _____

Lloji i njësisë kadastrale / Vrsta katastarske jedinice :

Parcel

Shkalla e zvoglimit / Razmerra plana : 1:1250

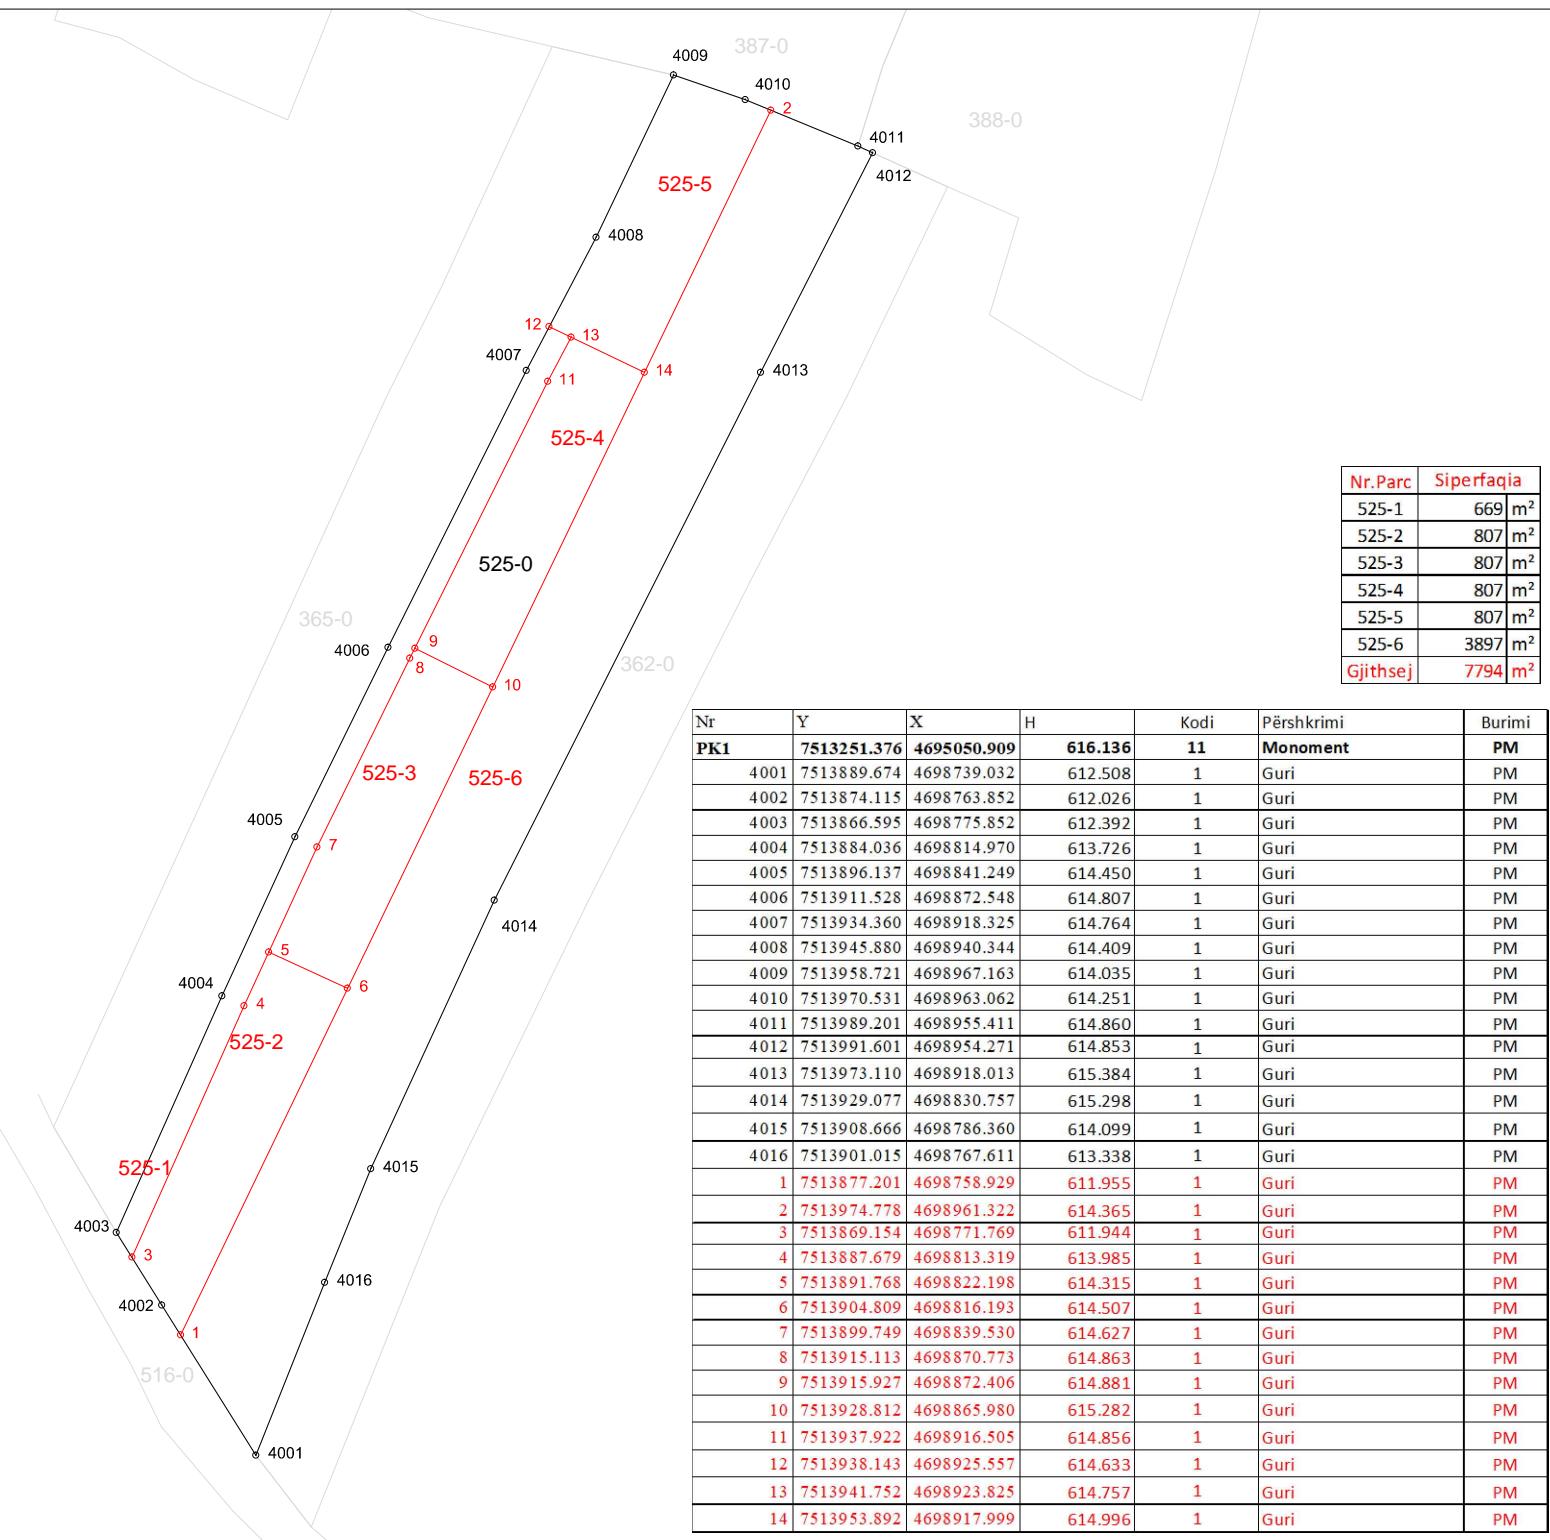

Rilevoi / Snimio: LIRIDON SEJDIU
 (emri dhe mbiemri i gjeddetit/kompanisë/ ime i prezime geodeta/ kompanije)

Nr. i licencës / Br. licence: 140

Nënshkrimi / Potpis:

Data e rilevimit / Datum snimanja: 22.08.2020

Aprovoi / Usvojio: _____
 (emri dhe mbiemri i pësonit zyrtar/ ime i prezime sluzbenog lica)

V.V.

Nënshkrimi / Potpis: _____

Data e aprovimit / Datum usvajanja: _____



Open Documents



525-0-PMuhaxereve

Point Id	Point Class	Date/Time	Easting	Northing	Ellip. Hgt.	Posn. + Hgt. Qlty
<input checked="" type="checkbox"/> A1	Measured	08/22/2020 08:41:50	7513877.2149	4698758.9316	611.9553	0.0154
<input checked="" type="checkbox"/> A2	Measured	08/22/2020 09:01:24	7513974.7637	4698961.3084	614.3648	0.0209
<input checked="" type="checkbox"/> A3	Measured	08/22/2020 09:30:54	7513869.1365	4698771.7554	611.9438	0.0171
<input checked="" type="checkbox"/> A4	Measured	08/22/2020 09:28:12	7513887.6833	4698813.3158	613.9854	0.0211
<input checked="" type="checkbox"/> A5	Measured	08/22/2020 09:23:52	7513891.7719	4698822.1986	614.3149	0.0183
<input checked="" type="checkbox"/> A6	Measured	08/22/2020 08:54:15	7513904.8388	4698816.1700	614.5069	0.0165
<input checked="" type="checkbox"/> A7	Measured	08/22/2020 09:20:29	7513899.7197	4698839.4584	614.6266	0.0629
<input checked="" type="checkbox"/> A8	Measured	08/22/2020 09:19:03	7513915.0913	4698870.7746	614.8628	0.0225
<input checked="" type="checkbox"/> A9	Measured	08/22/2020 09:16:42	7513915.9184	4698872.3883	614.8811	0.0234
<input checked="" type="checkbox"/> A10	Measured	08/22/2020 08:56:26	7513928.7994	4698865.9630	615.2822	0.0194
<input checked="" type="checkbox"/> A11	Measured	08/22/2020 09:51:12	7513937.8949	4698916.4904	614.8560	0.0213
<input checked="" type="checkbox"/> A12	Measured	08/22/2020 09:08:27	7513938.1670	4698925.5678	614.6326	0.0176
<input checked="" type="checkbox"/> A13	Measured	08/22/2020 09:09:59	7513941.7289	4698923.8287	614.7568	0.0249
<input checked="" type="checkbox"/> A14	Measured	08/22/2020 08:58:38	7513953.8832	4698917.9821	614.9965	0.0192
<input checked="" type="checkbox"/> A4001	Measured	08/22/2020 09:34:05	7513889.6676	4698739.0392	612.5079	0.0148
<input checked="" type="checkbox"/> A4002	Measured	08/22/2020 08:46:32	7513874.1205	4698763.8680	612.0259	0.1613
<input checked="" type="checkbox"/> A4003	Measured	08/22/2020 09:29:15	7513866.5952	4698775.8770	612.3918	0.0180
<input checked="" type="checkbox"/> A4004	Measured	08/22/2020 09:26:34	7513884.0621	4698814.9637	613.7256	0.0221
<input checked="" type="checkbox"/> A4005	Measured	08/22/2020 09:21:23	7513896.1517	4698841.2655	614.4504	0.0265
<input checked="" type="checkbox"/> A4006	Measured	08/22/2020 09:14:57	7513911.5159	4698872.5375	614.8074	0.0222
<input checked="" type="checkbox"/> A4007	Measured	08/22/2020 09:12:02	7513934.3856	4698918.3308	614.7637	0.0241
<input checked="" type="checkbox"/> A4009	Measured	08/22/2020 09:05:54	7513958.7320	4698967.1543	614.0347	0.0183
<input checked="" type="checkbox"/> A4010	Measured	08/22/2020 09:04:40	7513970.5340	4698963.0576	614.2512	0.0196
<input checked="" type="checkbox"/> A4011	Measured	08/22/2020 09:47:26	7513989.2100	4698955.3946	614.8605	0.0263
<input checked="" type="checkbox"/> A4012	Measured	08/22/2020 09:45:39	7513991.6138	4698954.2458	614.8526	0.0137
<input checked="" type="checkbox"/> A4013	Measured	08/22/2020 09:44:09	7513973.1163	4698918.0198	615.3839	0.0167
<input checked="" type="checkbox"/> A4014	Measured	08/22/2020 09:41:45	7513929.0663	4698830.7680	615.2981	0.0152
<input checked="" type="checkbox"/> A4015	Measured	08/22/2020 09:39:36	7513908.7055	4698786.3670	614.0988	0.0151
<input checked="" type="checkbox"/> A4016	Measured	08/22/2020 09:38:02	7513901.0235	4698767.6297	613.3385	0.0159
<input checked="" type="checkbox"/> B1	Measured	08/22/2020 09:55:41	7513877.1947	4698758.9208	612.0175	0.0214
<input checked="" type="checkbox"/> B10	Measured	08/22/2020 09:53:07	7513928.8183	4698865.9666	615.3042	0.0183
<input checked="" type="checkbox"/> B4004	Measured	08/22/2020 09:54:29	7513884.0174	4698814.9725	613.7184	0.0192
<input checked="" type="checkbox"/> B4009	Measured	08/22/2020 09:49:35	7513958.7190	4698967.1286	614.0609	0.0219
<input checked="" type="checkbox"/> PK1	Measured	08/22/2020 10:49:06	7513251.3762	4695050.9093	616.1364	0.0205
<input checked="" type="checkbox"/> RTCM-Ref 0049	Reference	08/22/2020 08:38:27	7513871.8727	4698791.3754	612.8449	0.0000
<input checked="" type="checkbox"/> RTCM-Ref 0052	Reference	08/22/2020 08:52:32	7513897.1963	4698806.8794	613.7209	0.0000
<input checked="" type="checkbox"/> RTCM-Ref 0105	Reference	08/22/2020 10:48:52	7513252.6448	4695050.8125	614.4729	0.0000



Republika e Kosovës

Republika Kosova - Republic of Kosovo

Qeveria e Kosovës - Vlada Kosova - Government of Kosovo

Ministria e Infrastrukturës dhe Ambientit/ Ministrastvo Infrastrukture i Sredine/ Ministry of Infrastructure and Environment

AGJENCIA KADASTRALE E KOSOVËS/ KOSOVSKA KATASTARSKA AGENCIJA/ KOSOVA CADASTRAL AGENCY

GJENDJA E VJETËR / STARO STANJE												GJENDJA E RE / NOVO STANJE								
Numri rendor, Redni broj	Komuna Opština	Zona kadastrale Katastarska zona	Mbiemri, Emri (Emri i Babës) Adresa e vendbanimit Prezime, Ime (Ime Oca) Adresa prebivališta 1. Pronar - Vlasnik - Owner 2. Posedues - Posednik - Possessor 3. Shfrytëzues - Korisnik - User	Nr. personal nga: Personalni Br. iz:	Nr. i Njësisë Br. Jedinice	1. (P) Parcela u/r 2. (O) Ndërtesa u/r Zgrada 3. (O) Pj. e ndërt. u/r Deo Zgrade	Kultura, klasa Shfrytëzimi aktual	□ □ □ 1. Adresa, Vend i quajtur Adresa, Zvano mesto 2. Infrastruktura Infrastruktura 3.Tjera karakterist.(referen ca) Ostale karakterist.(referen sa)	Përshkrimi i gjendjes së Njësisë Opis stanja Jedinice	Mbiemri, Emri (Emri i Babës) Adresa e vendbanimit Prezime, Ime (Ime Oca) Adresa prebivališta 1. Pronar - Vlasnik 2. Posedues - Posednik 3. Shfrytëzues - Korisnik	Nr. i Njësisë Br. Jedinice	1. (P) Parcela u/r 2. (O) Ndërtesa u/r Zgrada 3. (O) Pj. e ndërt. u/r Deo Zgrade	Kultura, klasa Shfrytëzimi aktual	Aktuelna upotreba	□ □ □	Dokumenti në të cilin bazohet ndërrimi dhe rezultati i shiqimit në vend të ngjarjes nga personi zyrtar për mirëmbajtjen e kadastrit.				
1	2	3	4	5	6	7	8	9	10	11	12	13	14	15	16	17				
1	Ferizaj	Prelez I Muhaxherëve	1	Sali (Isuf) Jakaj	1	1003798565	1	00525-0	R	Arë(2)	7794	Ranja Rruga Ferizajit	1	Sali (Isuf) Jakaj	1	00525-1 00525-2 00525-3 00525-4 00525-5 00525-6	Arë(2) Arë(2) Arë(2) Arë(2) Arë(2) Arë(2)	669 807 807 807 807 3897	Gjithësej	7794
Gjeodeti/kompania e licencuar: LIRIDON SEJDIU				Nr i licencës: 140								Nënshkrimi dhe vula:								



Republika e Kosovës
Republika Kosova-Republic of Kosovo
Qeveria e Kosovës- Vlada Kosova- Government of Kosovo
Ministria e Infrastrukturës dhe Ambientit/ Ministrastvo Infrastrukture i Sredine/ Ministry of Infrastructure and Environment
AGJENCIA KADASTRALE E KOSOVËS/KOSOVSKA KATASTARSKA AGENCIJA/ KOSOVO CADASTRAL AGENCY

Komuna: Ferizaj	Zona Kadastrale: Prelez i Muhxherëve
Numri i njësis kadastrale: 00525-0	Sistemi koordinat: KosovaRef01

Nr	Y	X	H	Kodi	Përshkrimi	Burimi
PK1	7513251.376	4695050.909	616.136	11	Monoment	PM
4001	7513889.674	4698739.032	612.508	1	Guri	PM
4002	7513874.115	4698763.852	612.026	1	Guri	PM
4003	7513866.595	4698775.852	612.392	1	Guri	PM
4004	7513884.036	4698814.970	613.726	1	Guri	PM
4005	7513896.137	4698841.249	614.450	1	Guri	PM
4006	7513911.528	4698872.548	614.807	1	Guri	PM
4007	7513934.360	4698918.325	614.764	1	Guri	PM
4008	7513945.880	4698940.344	614.409	1	Guri	PM
4009	7513958.721	4698967.163	614.035	1	Guri	PM
4010	7513970.531	4698963.062	614.251	1	Guri	PM
4011	7513989.201	4698955.411	614.860	1	Guri	PM
4012	7513991.601	4698954.271	614.853	1	Guri	PM
4013	7513973.110	4698918.013	615.384	1	Guri	PM
4014	7513929.077	4698830.757	615.298	1	Guri	PM
4015	7513908.666	4698786.360	614.099	1	Guri	PM
4016	7513901.015	4698767.611	613.338	1	Guri	PM
1	7513877.201	4698758.929	611.955	1	Guri	PM
2	7513974.778	4698961.322	614.365	1	Guri	PM
3	7513869.154	4698771.769	611.944	1	Guri	PM
4	7513887.679	4698813.319	613.985	1	Guri	PM
5	7513891.768	4698822.198	614.315	1	Guri	PM
6	7513904.809	4698816.193	614.507	1	Guri	PM
7	7513899.749	4698839.530	614.627	1	Guri	PM
8	7513915.113	4698870.773	614.863	1	Guri	PM
9	7513915.927	4698872.406	614.881	1	Guri	PM
10	7513928.812	4698865.980	615.282	1	Guri	PM
11	7513937.922	4698916.505	614.856	1	Guri	PM
12	7513938.143	4698925.557	614.633	1	Guri	PM
13	7513941.752	4698923.825	614.757	1	Guri	PM
14	7513953.892	4698917.999	614.996	1	Guri	PM

Matja e pikave në dy seri						
Seria	Nr. Pikës	Y	X	H	ΔY	ΔX
I	1	7513877.22	4698758.93	611.96	0.0200	0.0110
II	1	7513877.20	4698758.92	612.02	-0.0190	-0.0040
I	10	7513928.799	4698865.963	615.28	0.0450	-0.0090
II	10	7513928.818	4698865.967	615.30	0.0130	0.0250
I	4004	7513884.062	4698814.964	613.73		0.0459
II	4004	7513884.017	4698814.973	613.72		0.0282
I	4009	7513958.732	4698967.154	614.03		
II	4009	7513958.719	4698967.129	614.06		

Koordinatat përfundimtare			
Nr	Y	X	H
1	7513877.205	4698758.927	611.986
10	7513928.809	4698865.965	615.293
4004	7513884.040	4698814.969	613.722
4009	7513958.726	4698967.142	614.048

Gjeodeti / Kompania gjeodete e licencuar:	LIRIDON SEJDIU	Nënshkrimi dhe vula:	
Numri i licencës	140		



Republika e Kosovës
Republika Kosova-Republic of Kosovo
Qeveria e Kosovës- Vlada Kosova- Government of Kosovo

Ministria e Infrastrukturës dhe Ambientit/ Ministrastvo Infrastrukture i Sredine/ Ministry of Infrastructure and Environment

AGJENCIA KADASTRALE E KOSOVËS/KOSOVSKA KATASTARSKA AGENCIJA/ KOSOVO CADASTRAL AGENCY

FORMULARI PËR KORIGJIMIN E SIPËRFAQËS

Gjeodeti / Kompania gjeodete e licencuar: Liridon Sejdiu	Numri i licencës:140
Komuna: Ferizaj	Zona Kadastrale: Prelez i Muhaxherëve
Numri i njësisë kadastrale: 00525-0	Numri i lëndës: 188/2020

1. Tabela e ndryshimeve të sipërfaqes

Numri i parcelës	Sipërfaqja faktike (m ²)	Sipërfaqja nga SIKTK-T (m ²)	Ndryshimi (m ²)	Sipërfaqja e korrigjuar (m ²)
00525-0	7794	7785	9	7794

Bazuar në procesverbalin e terrenit, pronarët janë pajtuar me pikat definitive kufitare të vendosura në terren nga të cilat edhe është derivuar sipërfaqja definitive që regjistrohet në SIKTK.

Nënshkrimi dhe vula e gjodetit: _____

Data: _____



Republika e Kosovës
Republika Kosova-Republic of Kosovo
Qeveria e Kosovës- Vlada Kosova- Government of Kosovo

Ministria e Infrastrukturës dhe Ambientit/ Ministrastvo Infrastrukture i Sredine/ Ministry of Infrastructure and Environment

AGJENCIA KADASTRALE E KOSOVËS/KOSOVSKA KATASTARSKA AGENCIJA/ KOSOVO CADASTRAL AGENCY

RAPORTI TEKNIK

Gjeodeti / Kompania gjeodete e licencuar: Liridon Sejdiu	Numri i licencës: 140
Komuna: Ferizaj	Zona Kadastrale: Prelez i Muhaxherëve
Numri i njësisë kadastrale: 00525-0	Lloji i lëndës: Ndarje e parcelës

Bazuar në kërkesën e palës **Mehdi (Isuf) Jakaj** me numër personal **1003798352** të parashtruar me datën **21.08.2020**, është bërë kërkesa për marrjen e produkteve kadastrale në Zyrën Kadastrale Komunale **Ferizaj** me datë **21.08.2020**. Pas analizimit të të dhënave me datë **22.08.2020** janë realizuar matjet në terren, për (**ndarjen/bashkimin**) e parcelave bazuar në (**gjendjen faktike/sipërfaqe të barazuara**).

Matjet në terren janë realizuar me instrument (GPS Leica 1230), ku fillimisht është bërë matja e pikës kontrolluese **PK1(pike e rrredit III)** pastaj matjet janë realizuar bazuar në kornizën AKK nr.: 2020/01

Matje të dyfishta kontrolluese janë realizuar në pikat numër **1,10,4004,4009**

Sfidat gjatë realizimit të

matjeve: _____

Matje të dyfishta kontrolluese janë realizuar në pikat numër **1,10,4004,4009**.

Raporti në formë tabelare:

Parcela para ndarjes/bashkimit	Sipërfaqja (m ²)	Korigjimi i sipërfaqe (po/jo)	Parcela pas ndarjes/bashkimit	Sipërfaqja (m ²)
00525-0	7794	po	00525-1	669
			00525-2	807
			00525-3	807
			00525-4	807
			00525-5	807
			00525-6	3897

Nënshkrimi dhe vula e gjodetit: _____

Data: _____